U

Skala 1 : 2000

Nama Pemohon	:	Arry Wibowo
Desa/Kelurahan	:	rungkut kidul
Kecamatan	:	rungkut
Kabupaten	:	surabaya
Propinsi	:	Jawa Timur
Luas	:	87107.32 M2
Titik tengah	:	112.4702.563, -7.1942.233

LEGENDA

00000 : Nomor Identifikasi Bidang Tan

Dipindai dengan CamScanner

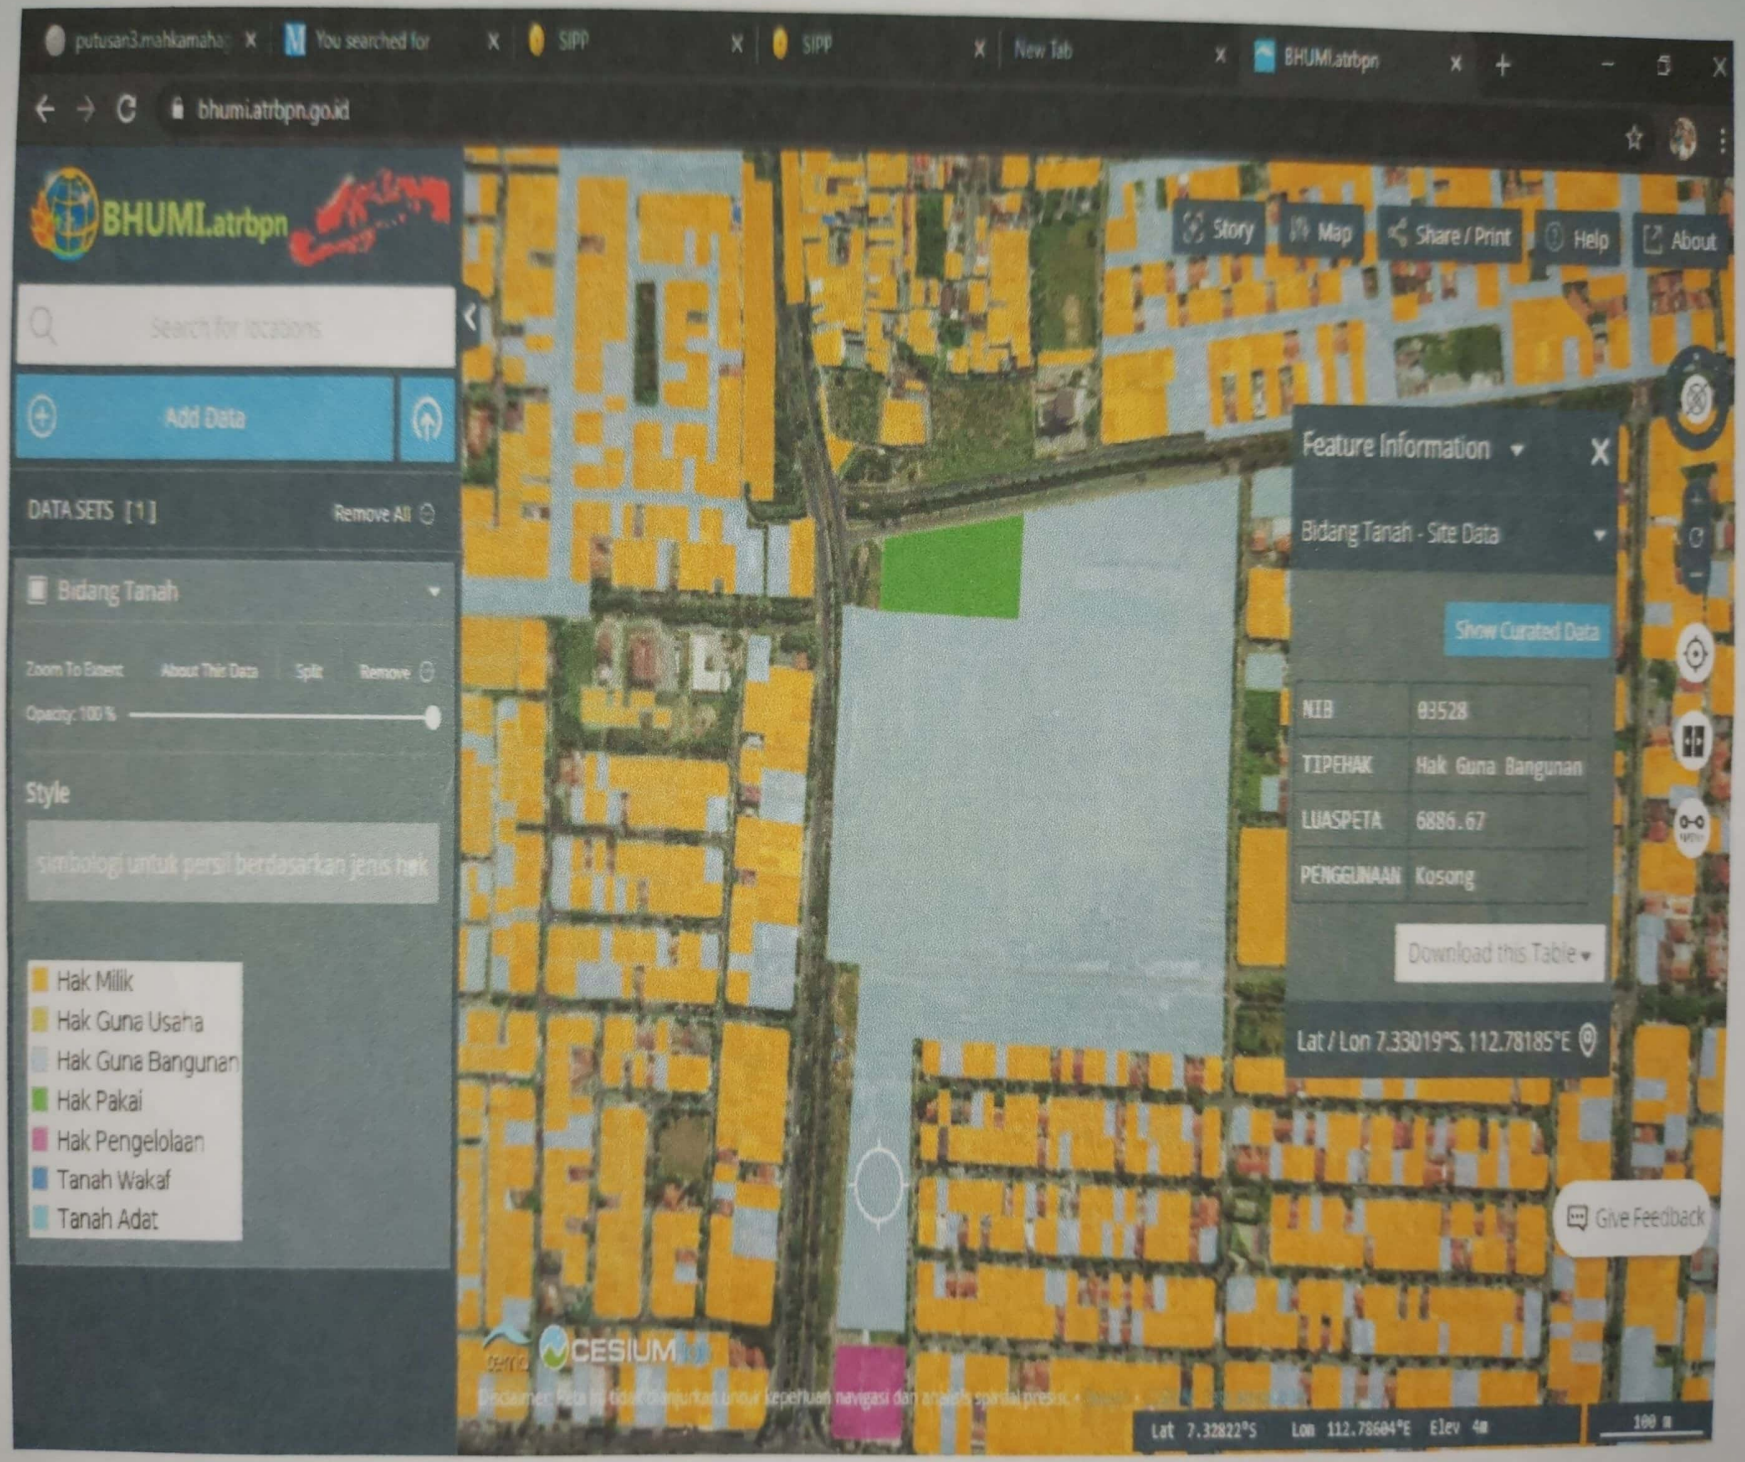

Dipindai dengan CamScanner

TERJEMAHAN

Sworn Translator
Penerjemah Tersumpah
Address : Mojokiangguru Kidul E-23 (III-42) Surabaya
Phone/Fax : (031)5993062 / 5310475

Akte Mengenai Hak Milik

Perponding no. 1523 no. 243, menurut akte Hak Milik/eigendom tertanggal 11 April yang telah dibuat oleh pejabat yang berwenang di Surabaya,
Terletak di Residensi Surabaya, di kantor di luar kantor Kadaster di Residensi Surabaya;

Di bagian sebelah Barat, bagian perkampunagn Desa Gunung Anyar di Surabaya, dan menurut perponding maka dimulai 1.800 Gulden ;

Pribumi : Nji Mas Siti Aminah
alias Nji Mas Entjeh (Osah)

Diangkat di Surabaya, notaris FRITS LAOW, notaris residensi Surabaya, sebagai seorang yang bertindak secara sepihak yang dalam waktu satu bulan telah memenuhi tentang pendaftaran mengenai persil-persil Hak Milik/eigendom tersebut. Yang tersebut di atas bertempat tinggal di Desa Goenoeng Anyar di Surabaya

Surabaya, tanggal 8 Juni 1931
Pegawai Pendaftaran
Tanah Tersumpah, Kelas 2

Turunan no. 243
Notaris Frits Laow di Surabaya
(stempel dan paraf)

Surabaya, 26 Agustus 2015.
Diterjemahkan oleh
IHK Sworn Translator

SWORN TRANSLATOR Penerjemah Tersumpah IHK Ir. Pratiwi Putri Tjahjono

Ir. Pratiwi Putri Tjahjono
Penerjemah Tersumpah Berdasarkan Surat Keputusan Gubernur Jawa Timur Nomor 188/106/KPTS/013/2003 tanggal 29 April 2003.
Terdaftar di Kedutaan Amerika - Surabaya

Dipindai dengan CamScanner

Sworn Translator
Penerjemah Tersumpah
Address : Majokangguru Kidul E-23 (III-42) Surabaya
Phone/Fax : (031)5993082 / 5310475

AHAN

Cetak di atas kertas Zegel 1931

SURAT UKUR :

Mengenai persil yang terletak di Residensi Surabaya. Bagian lapangan sebelah Timur dari Nji Mas Siti Aminah alias Nji Mas Entjeh (Osah), keluarga.

Perponding no. 1523

Tempatnya :
Desa Gunung Anyar
Di Surabaya

Pajak 1800 Gulden

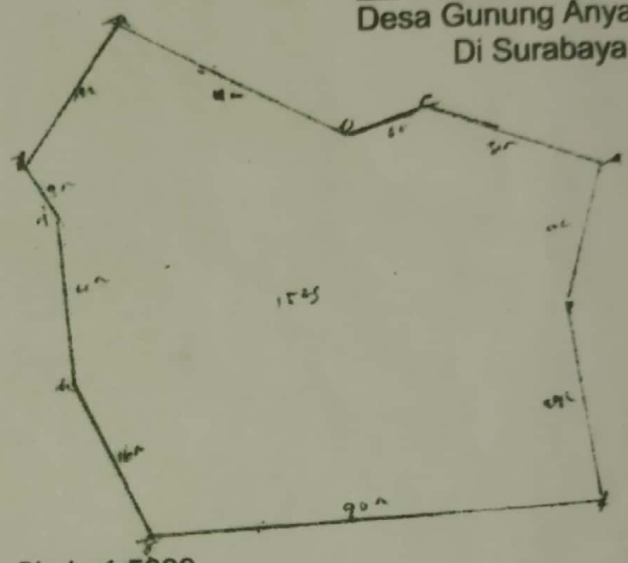

Skala 1:5000
Keterangan / Uraian
SEBIDANG TANAH KEBON
BERBATASAN

Di sebelah Utara : persil di desa Gunung Anyar di Surabaya
Di sebelah Selatan : persil perponding No. 2011
Di sebelah Timur : persil perponding No. -
Di sebelah Barat : berbatasan pada saluran air

Ukuran

Di sebelah Utara : }
Di sebelah Selatan : } lihat gambar alias
Di sebelah Timur : }
Di sebelah Barat : }

Persil tersebut mempunyai ukuran 80.857m2
Sehubungan dengan akte tertanggal 14 Juni 1914 no. 108, dimiliki orang pribumi Nji Mas Siti Aminah alias Nji Mas Entjeh (Osah). Surat Ukur ini sebagai gantinya untuk Surat Ukur – surat ukur yang telah dibuat untuk persil tersebut.

Surabaya, 8 Juni 1931
Yang berhak menyimpan dari Kantor Kadaster

Turunan No. 243
Biaya : 45 Gulden
Zegel : 1,50 Gulden
Biaya dan Registrasi : no. 165

SWORN TRANSLATOR
Penerjemah Tersumpah
iHK
A. Rodiwi Putri Tjahjono

Dipindai dengan CamScanner

SURAT PERNYATAAN

Yang bertanda tangan dibawah ini,

N I K	: 3205051704590002
Nama lengkap	: CHEPY SUHENDI
Pekerjaan	: Swasta
Alamat tempat tinggal	: Komp. Pataruman Indah Blok. B-45 RT. 003 / RW. 008 Kelurahan Desa Pataruman Kecamatan Tarogong Kidul Kab.Garut.

Bertindak untuk diri sendiri dan untuk atas nama seluruh ahli waris " NYIMAS ENTJEH alias NYIMAS SITI AMINAH alias OSAH YUSTINA REGEN binti MAS TAKARAMA alias H. SYUKUR, berdasarkan PENGADILAN AGAMA KELAS IB CIANJUR Nomor : 44/Pdt.P/2008/PA.Cjr. Tanggal : 07 April 2008, dan Berdasarkan Akta nomor 2 Tanggal : 11 Oktober 2011 (Surat Kuasa Substitusi) Notaris : HASNA LASTRY S.H. MKn. .....
Selaku pemilik yang sah atas Hak Milik Eigendom Verponding no. 1523 / no. 243 di Desa G0enoeng Anyar, Surabaya – Propinsi Jawa Timur. .....

Dengan ini menyatakan sebagai berikut ;

1. Bahwa benar kami Ahli Waris yang Sah atas Tanah Perceel Hak Milik ex Eigendom Verponding No.1523 / no. 243 atas nama NYI MAS ENTJEH alias NYIMAS SITI AMINAH alias OSAH YUSTINA binti MAS TAKARAMA alias H. SYUKUR, seluas 80.857 M2 yang terletak di Desa Goenoeng Anyar Surabaya Propinsi Jawa Timur .....
2. Bahwa benar hingga sampai saat ini kami belum pernah menjual, mengoper Alihkan, memindah tangankan, menjaminkan, menggadaikan, dan atau melepaskan Hak, Tanah Perceel ex Eigendom verponding nomor : 1523 / No. 243 atas nama NYI MAS ENTJEH alias NYI MAS SITI AMINAH alias OSAH YUSTINA REGEN binti MAS TAKARAMA alias H, SYUKUR tanah seluas 80.857 M2 yang terletak di Desa Goenoeng Anyar Surabaya Propinsi Jawa Timur .....
3. Bahwa benar kami selaku Ahli Waris dan Pemilik yang Sah, atas Hak Tanah Perceel ex Eigendom Verponding Nomor : 1523 / No. 243 sebagamana tersebut diatas, belum pernah menerima Ganti Rugi, Kompensasi, dan atau dalam bentuk apapun, baik dari Pemerintah maupun Pihak Swasta atas pemanfaatan, penguasaan, dan penggunaan atas Hak Tanah tanah Perceel ex Eigendom Verponding nomor : 1523 / No. 243 milik kami tersebut diatas ....

Demikian Surat Pernyataan ini dibuat dan diterbitkan hanya berlaku untuk kepentingan tersebut diatas agar dipergunakan sebagaimana mestinya, ber-integritas dengan kebenaran, taat hukum serta penuh rasa tanggung jawab .....

Bandung, tanggal : 29 Agustus 2012

Yang membuat Pernyataan
A/n Seluruh Ahli Waris
NYI MAS ENTJEH AITI AMINAH

Hormat kami

METERAI TEMPEL
833A8ABF256193309
ENAM RIBU RUPIAH
6000 DJP

CHEPY SUHENDI

Dipindai dengan CamScanner

Dengan demikian kepemilikannya adalah syah berdasarkan hukum

- Berdasarkan UU Nomor 1 Tahun 1958 tersebut, hingga karenanya sejak tanggal 24 Januari 1958 secara sendirinya menjadi tanah negara, namun de facto belum, karena tindakan selanjutnya oleh pemerintah terhadap obyek tanah R.V. Eigendong Verponding harus :
  - Ditegaskan berdasarkan SK Menteri Agraris, yang harus disampaikan kepada Eigenaar/Pemilik R.V. Eigendong Verponding melalui juru sita Pengadilan Negeri yang selanjutnya dicatat oleh Kadaster/BPN dan diumumkan dalam berita negara;
  - Sesuai dengan UU 1/Tahun 1958 dan Keppres No. 32/1979, bahwa ahli waris diberikan ganti rugi atas tanah tersebut;
  - Bahwa dengan kondisi di atas, tanah tersebut dikembalikan kepada Ahli Waris Nyimas Entjeh Siti Aminah/NV. Blomkring, berdasarkan R.V. Eigendom Verponding Nommer 1623 yang terletak di Kampoeng GOENOENG ANJAR, Distict Soerabaja, Bestuurafdeling Soerabaja.
  - Eks tanah Eigendom Verponding dapat diberikan hak baru baik berupa HGB, HGP, atau Hak Pengelolaan.
  - Dijadikan sebagai Tanah yang dikuasai negara bila luasnya di atas 10 bahu/7.180m2, Menurut Undang-Undang No. 1/1958.

Dipindai dengan CamScanner

MEETBRIEF :

Van het Perceel gelegen i
in de Residentie Soerabaja,
Afdeeling het Oosterveld en
Nji Mas Siti Aminah en Nji Ma
Entjeh (Osah), familie Buite
Kadas ter;

Verponding :

No : 1 5 2 3

Taxatie : f.1800,-

Buurt of Wijk : Desa GOENOENG ANJAR, e
Soerabaja;

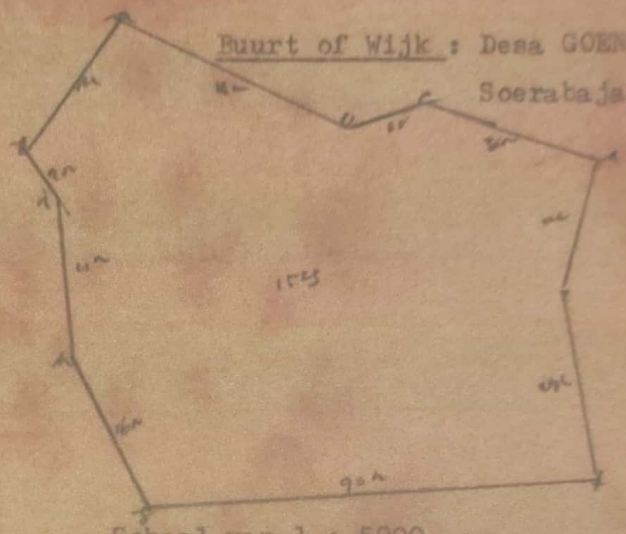

Schaal van 1 : 5000

O M S C H R I J V I N G

Een Stuk Tuin Land

B E L E N D I N G E N :

Ten Noorden aan het Perceel van Desa Goenoeng Anjar, en Soerabaja;
" Zuiden aan het perceel en verponding no.2011
" Oosten aan het perceel en verponding no. -
" Westen aan de Spruitje,

A F M E T I N G E N :

Aan de Noordzijde)
Aan de Zuidzijde)
Aan de Oostzijde) Zie de teekening;
Aan de Westzijde)

Voornoemd perceel heeft gene inlanvlokteson 80.857 M2, een behoort ingevolge acte dd.14 Djoeni 1914.no.108.aan de Inlander NJI MAS SITI AMINAH en NJI MAS ENTJEH (OSAH), Deze meetbrief stukter vervonging van voor leden opgemaakte meetbriefen van dit perceel.

Afschrift : No.243.

Soerabaja, den 8 Djoeni 193

Kosten : f.45,-
Zegel : f. 1,50
Salaris en Registr : No.165

De Bewaarder van Het Kadaster.

ACTE VAN EIGENDOM :

Verponding no.1523.no.243,blijkens acte eigendom op den elsten April,voor-
de deer toe bevoegde autoriteiten te Soerabaja,verleden; ----------
gelegen in de residentie Soerabaja,bertuursafdeeling district buiten eenige
kadastrale afdeeling deresidentie te Soerabaja; ----------
in het Westerveld,buurt of Wijk : Desa Goenoeng Anjar, en Soerabaja; -------
en bij het middel der verponding,zijn geheel aangelagen over eene waarde -
f.1800,-; ----------

Inlander : NJI MAS SITI AMINAH en NJI MAS ENTJEH (OSAH);

to benoemm den te Soerabaja,residenrenden Notaris RRITS LAOW ; ----------
wiens en els enzidig persoon wiens die vurdeeling binnen een maand nadat -
de openbare van voor achbraven eigendom perceelen geheel zal toe stand -
gebracht; ----------
De hierveren genoemd wonende in de Desa Goenoeng Anjar, te Soerabaja; ----

Soerabaja, den 8 Djoeni 1931

De Gezweren Landmeter der 2de Klasje.

Afschrift : No.243.

Notaris,
FRITS LAOW,
te
S O E R A B A J A.

Dipindai dengan CamScanner

Koetipan :

INLANDS VERPONDING JAITOE PADJEG TANAH DAN ROEMAH.

4 tahoen hingga 1944.

No.1523.daftar bilangan padjeg.

Residentie :)
Regenchap :) Soerabaja.
District :)
Wijk :) GOENOENG ANJAR,
Desa :)

SOERAT PADJEG.

(tertjatat pada hari boelan 7 Maart 1944)

Keterangan tempat doedoeknja tana atau pekarangan di;

GOENOENG ANJAR; ----------

Namanja orang jang kena padjeg dan tempat tinggalnja : NJI MAS SITI AMINAN -en NJI MAS ENTJEH (OSAH); Goenoeng Anjar wijk Goenoeng Anjar; ----------

Djoemlah padjeg setiap boelan f.9,05

Soerabaja,den 7 Maart '44

Salinan njang sama boenjinja,

Notaris,

FRITS IACW,

te

SOERABAJA.

Kantor,

PADJEG TANAH DAN ROEMAH

ttd.tjap

SOERABAJA.

Dipindai dengan CamScanner

S A L I N A N : Riwajat singkat tana perceel verponding nomer 1523, jang terletak di Desa GOENOENG ANJAR en SOERABAJA:

Pada hari ini Raboe tanggal 21 Djoeli 1899, FAN DER CLERK, selakoe komi COUVERDEMENT VAN NEDERLANDS INDIE, jang berkedoedoekan di Soerabaja; ----- Oentoek itoe mengakoe dimoeka Toean Notaris FRITS LAOW, te Soerabaja; ----- bahoewa itoe perceel verponding nomer 1523, jang loeasnja kira-kira 80.857 M2.(delapanpoeloeh riboe delapanratoes limapoeloeh toedjoeh meter); ------ sesoeai perdjandjian njang diboeat dihadapan Toean Notaris, te Soerabaja, dan atas nama terseboet diatas, njang mana milik peroesahaan dan soedah di daftarkan di Kantor Kadaster te Soerabaja, njang soedah di soempah kelas - 2(doea), dan soedah bajar padjaknja sebesar f.21,-(doeapoeloeh satoe perak -dan moelai hari ini soedah mendjadi miliknja sendiri bernama NJI MAS SITI AMINAH en NJI MAS ENTJEH (OSAH); ----------

-----Tjoekoep sekean riwajat singkat tana perceel verponding nomer 1523, jang terletak di Desa Goenoeng Anjar, te Soerabaja; --------- ----------

Oentoek digoenakan sebagaimana mestinja dikemoedian hari: ----------

Soerabaja, den 21 Djoeli 1899,
Tanda tangan.tjap
te
FAN DER CLERK.

---

komist.COUVERDEMENT VAN NEDERLANDS INDIE.

Soerabaja, den 7 Mei 1931
Didaftarkan di Kantor ~~Kadaster,~~
Raad Van Justitie,
No.22.tanggal 7 Mei 1931
RAAD VAN JUSTITIE,
te
S O E R A B A J A.

Salinan njang sama boenjinja,
No.7.Not.tanggal 2 Mei 1931
Notaris,
FRITS LAOW,
te
S O E R A B A J A.

Dipindai dengan CamScanner